



ARCHITECTURAL PORTFOLIO

JOMARIE E. LADORES




4 BEDROOMS

BUNGALOW



MODERN RESIDENTIAL

TWO-STOREY

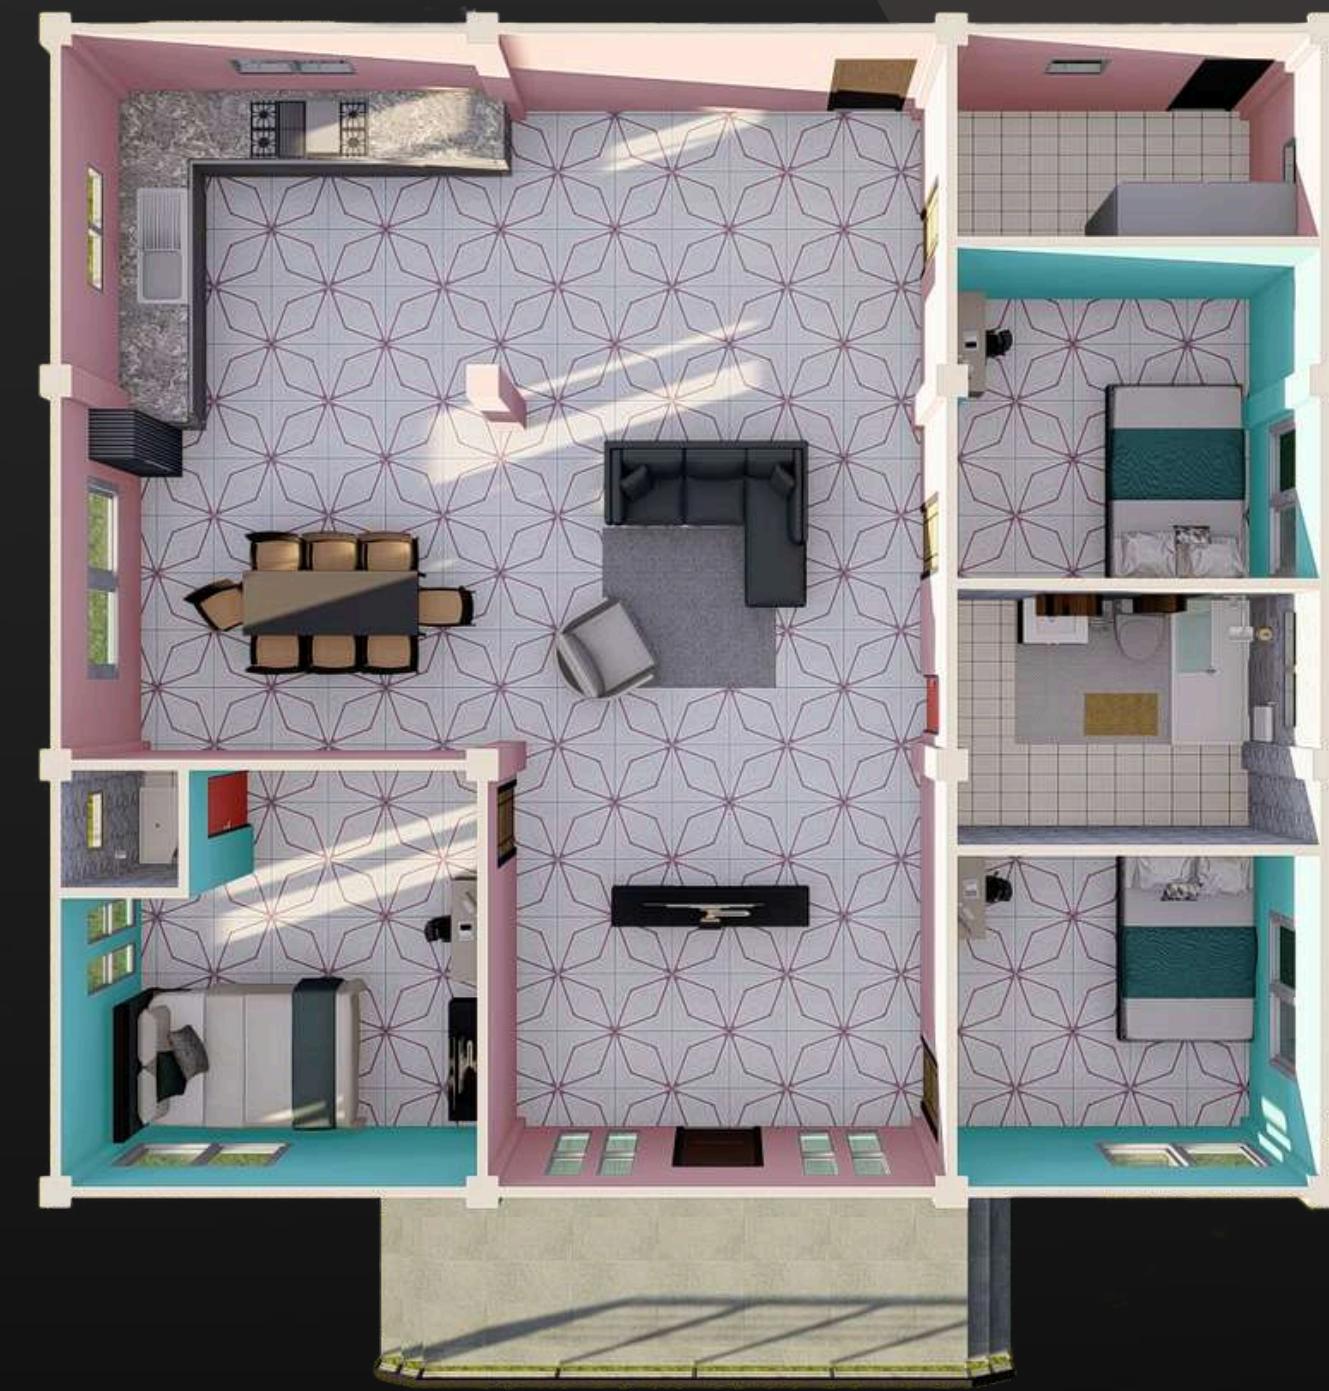

3 BEDROOMS

BUNGALOW




SIDE BY SIDE DUPLEX

TWO-STORY



STANDARD DUPLEX

TWO-STOREY

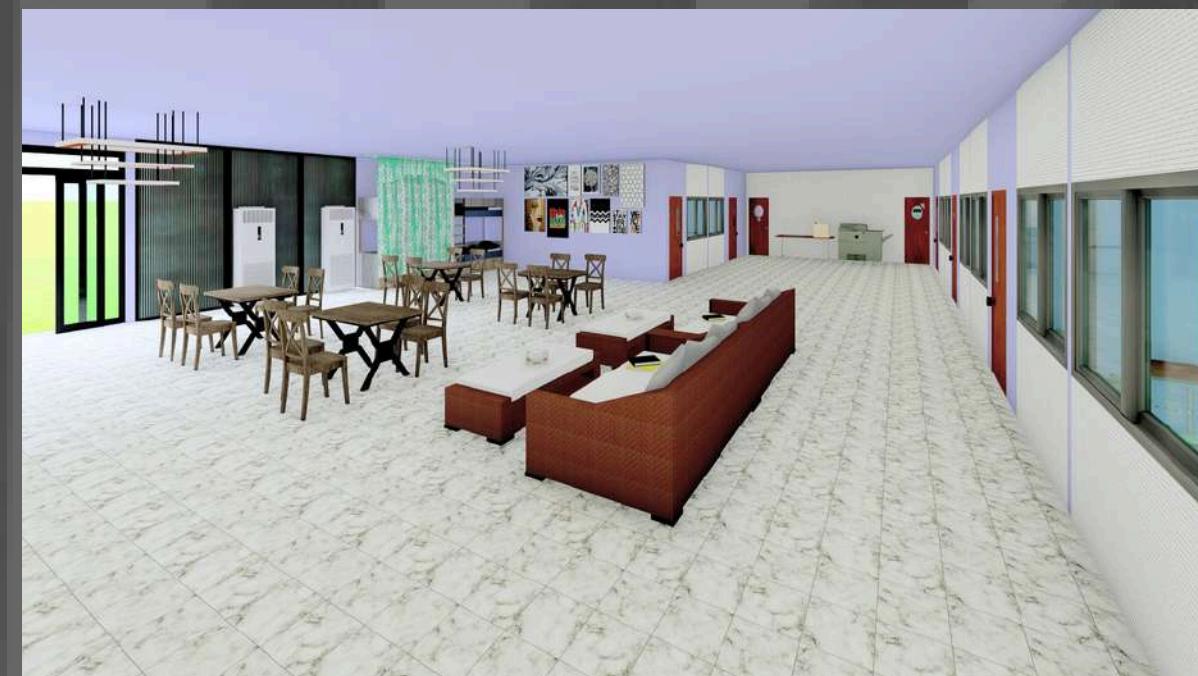

SEMI-COMMERCIAL


TWO-STOREY



SINGLE-ATTACHED

TWO-STORY



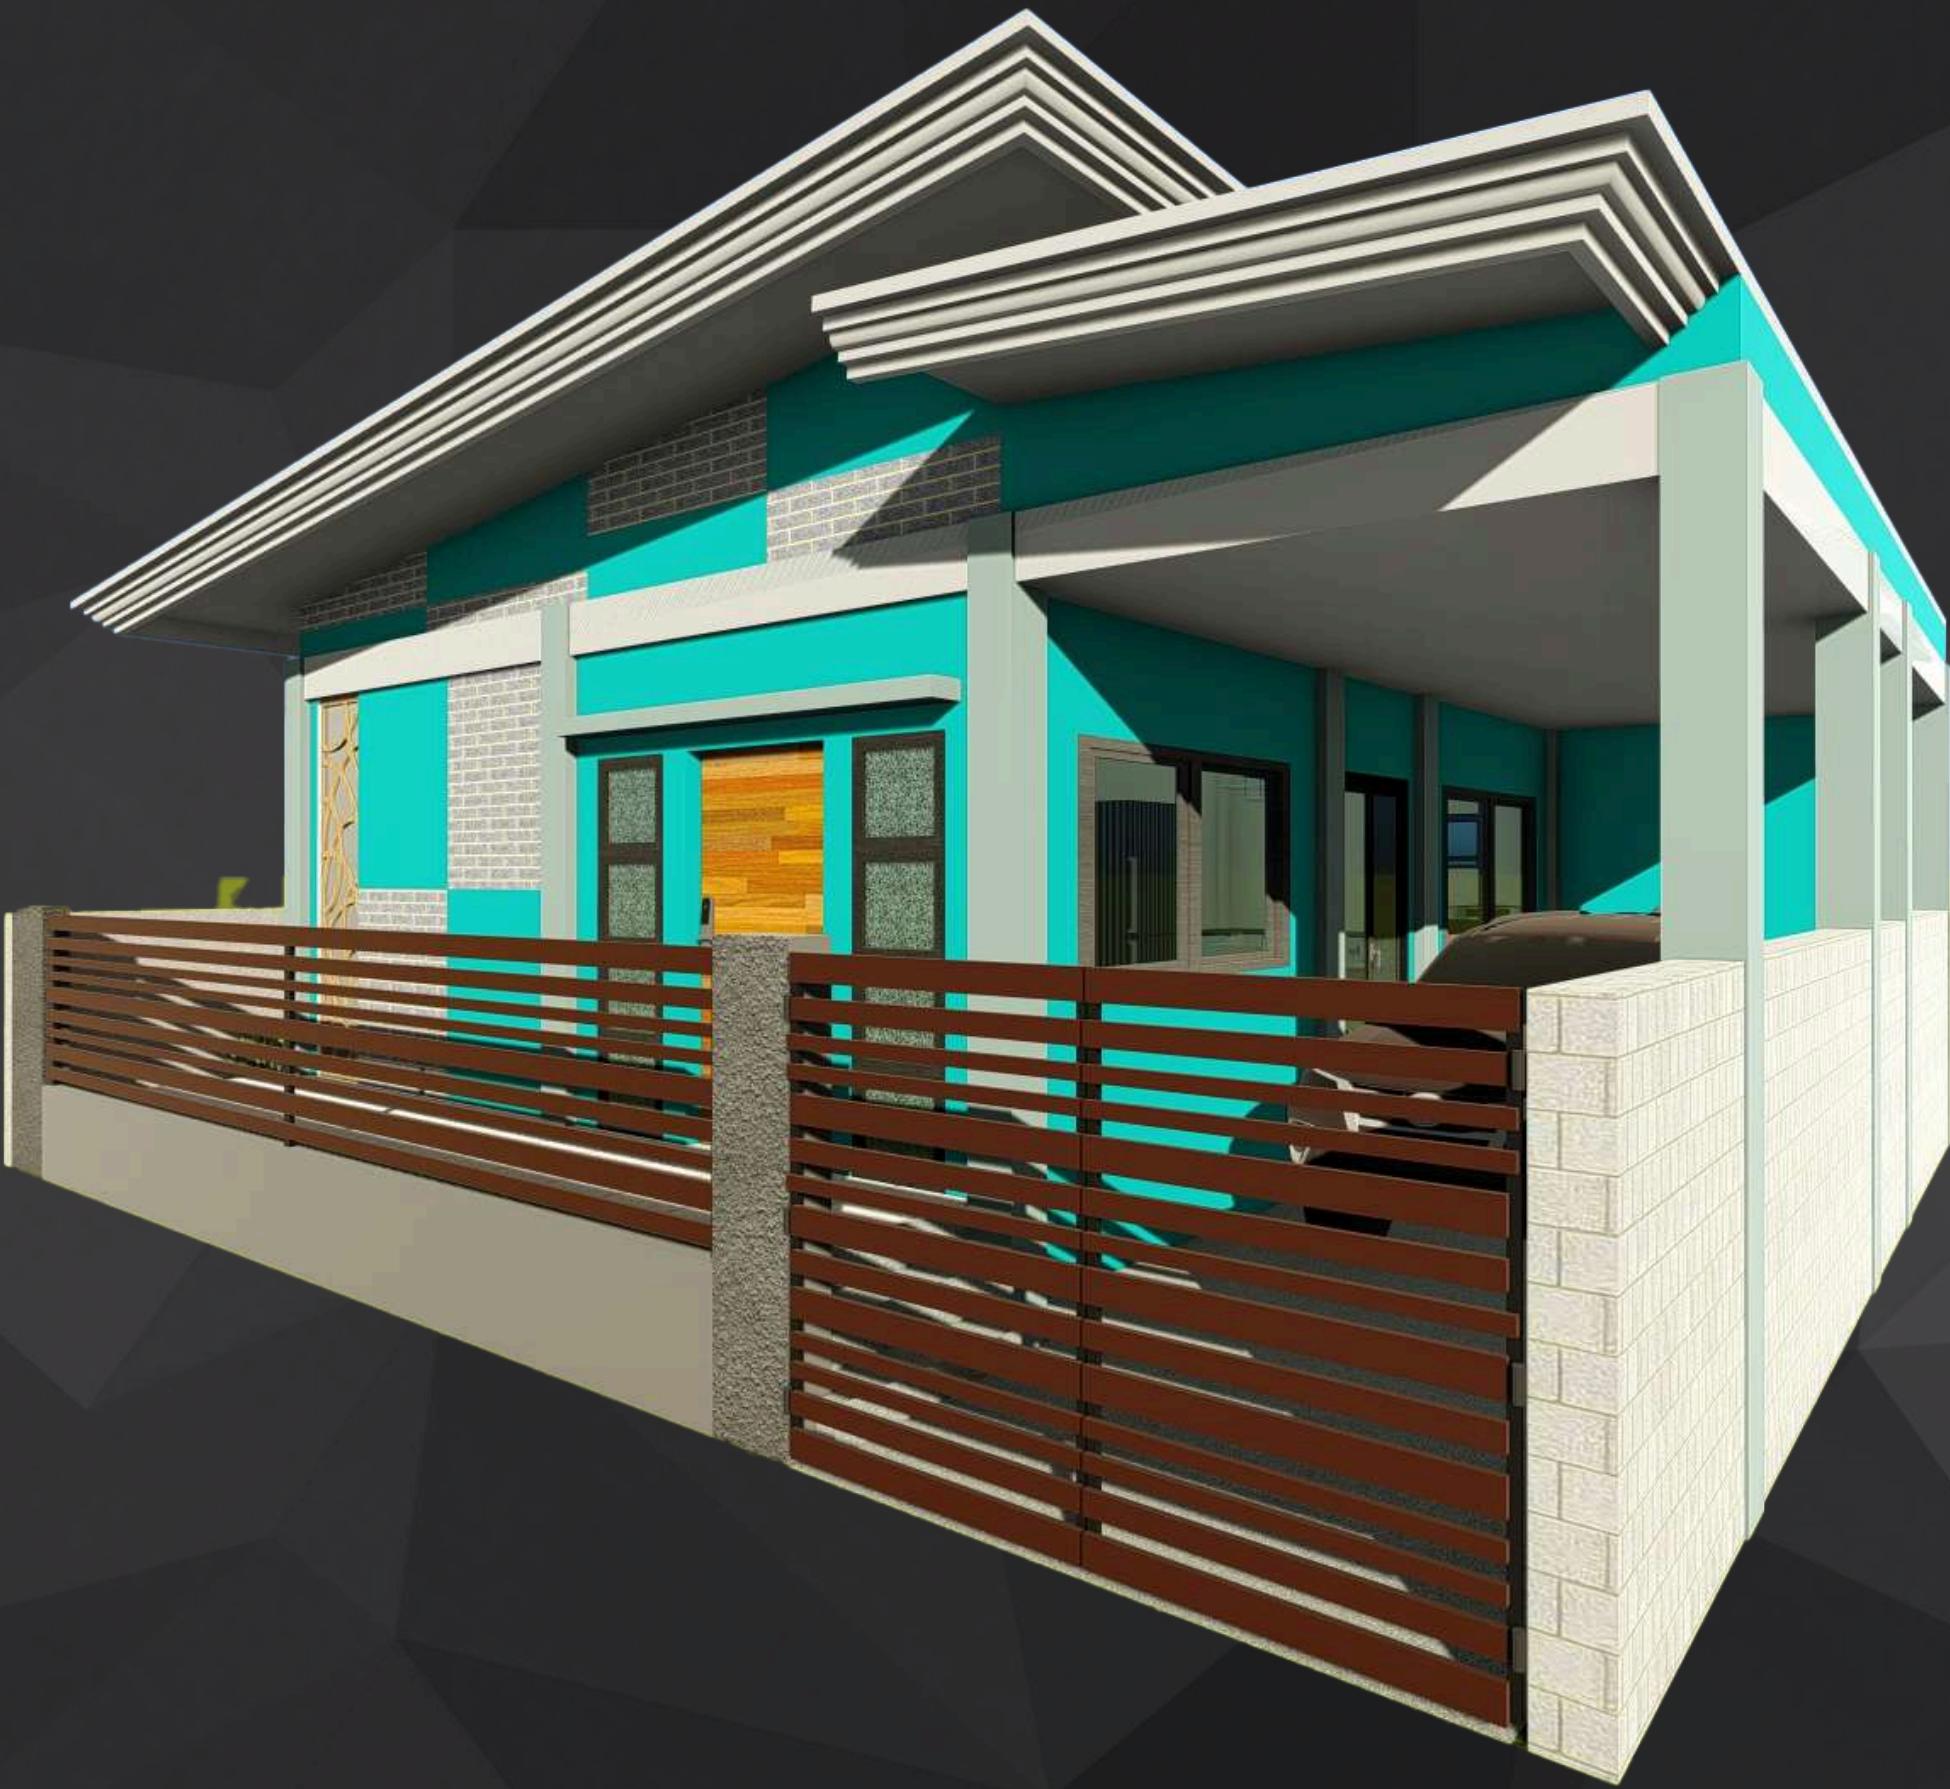


MODERN

TWO-STOREY






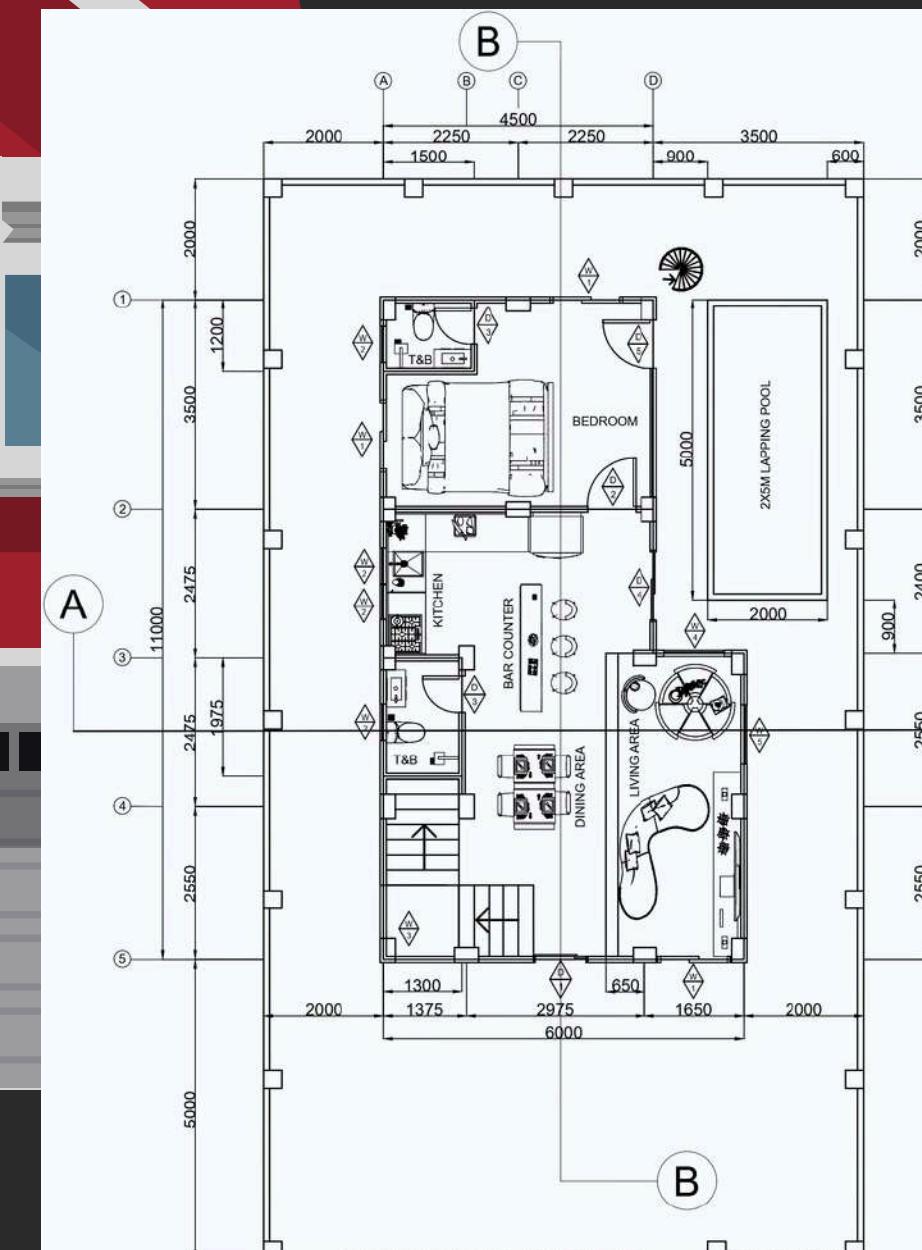




FIRST FLOOR PLAN

SCALE 1:1000

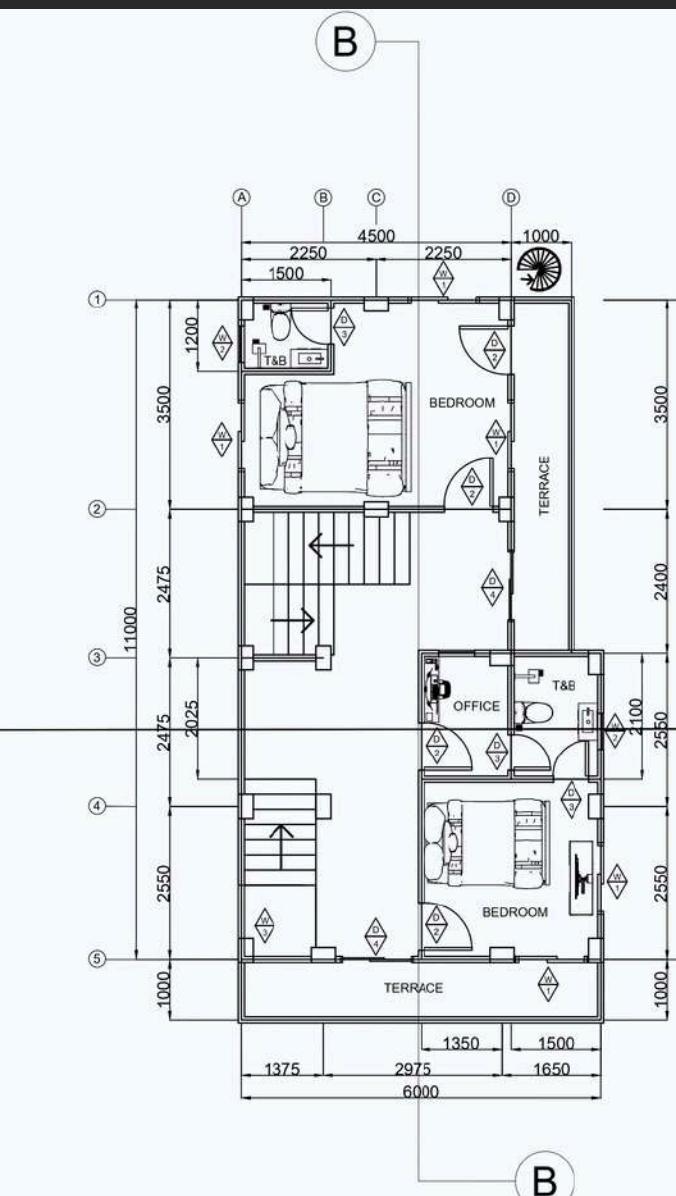


SECOND FLOOR PLAN
SCALE 1:1000




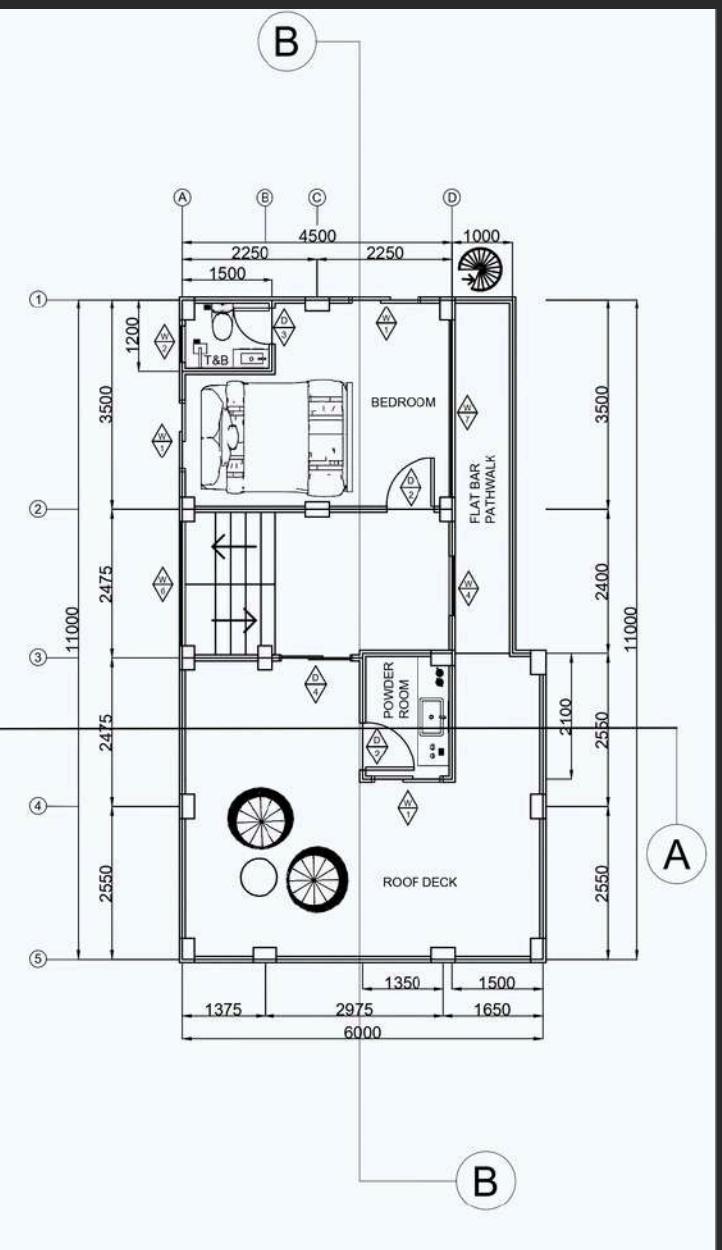


THIRD FLOOR PLAN





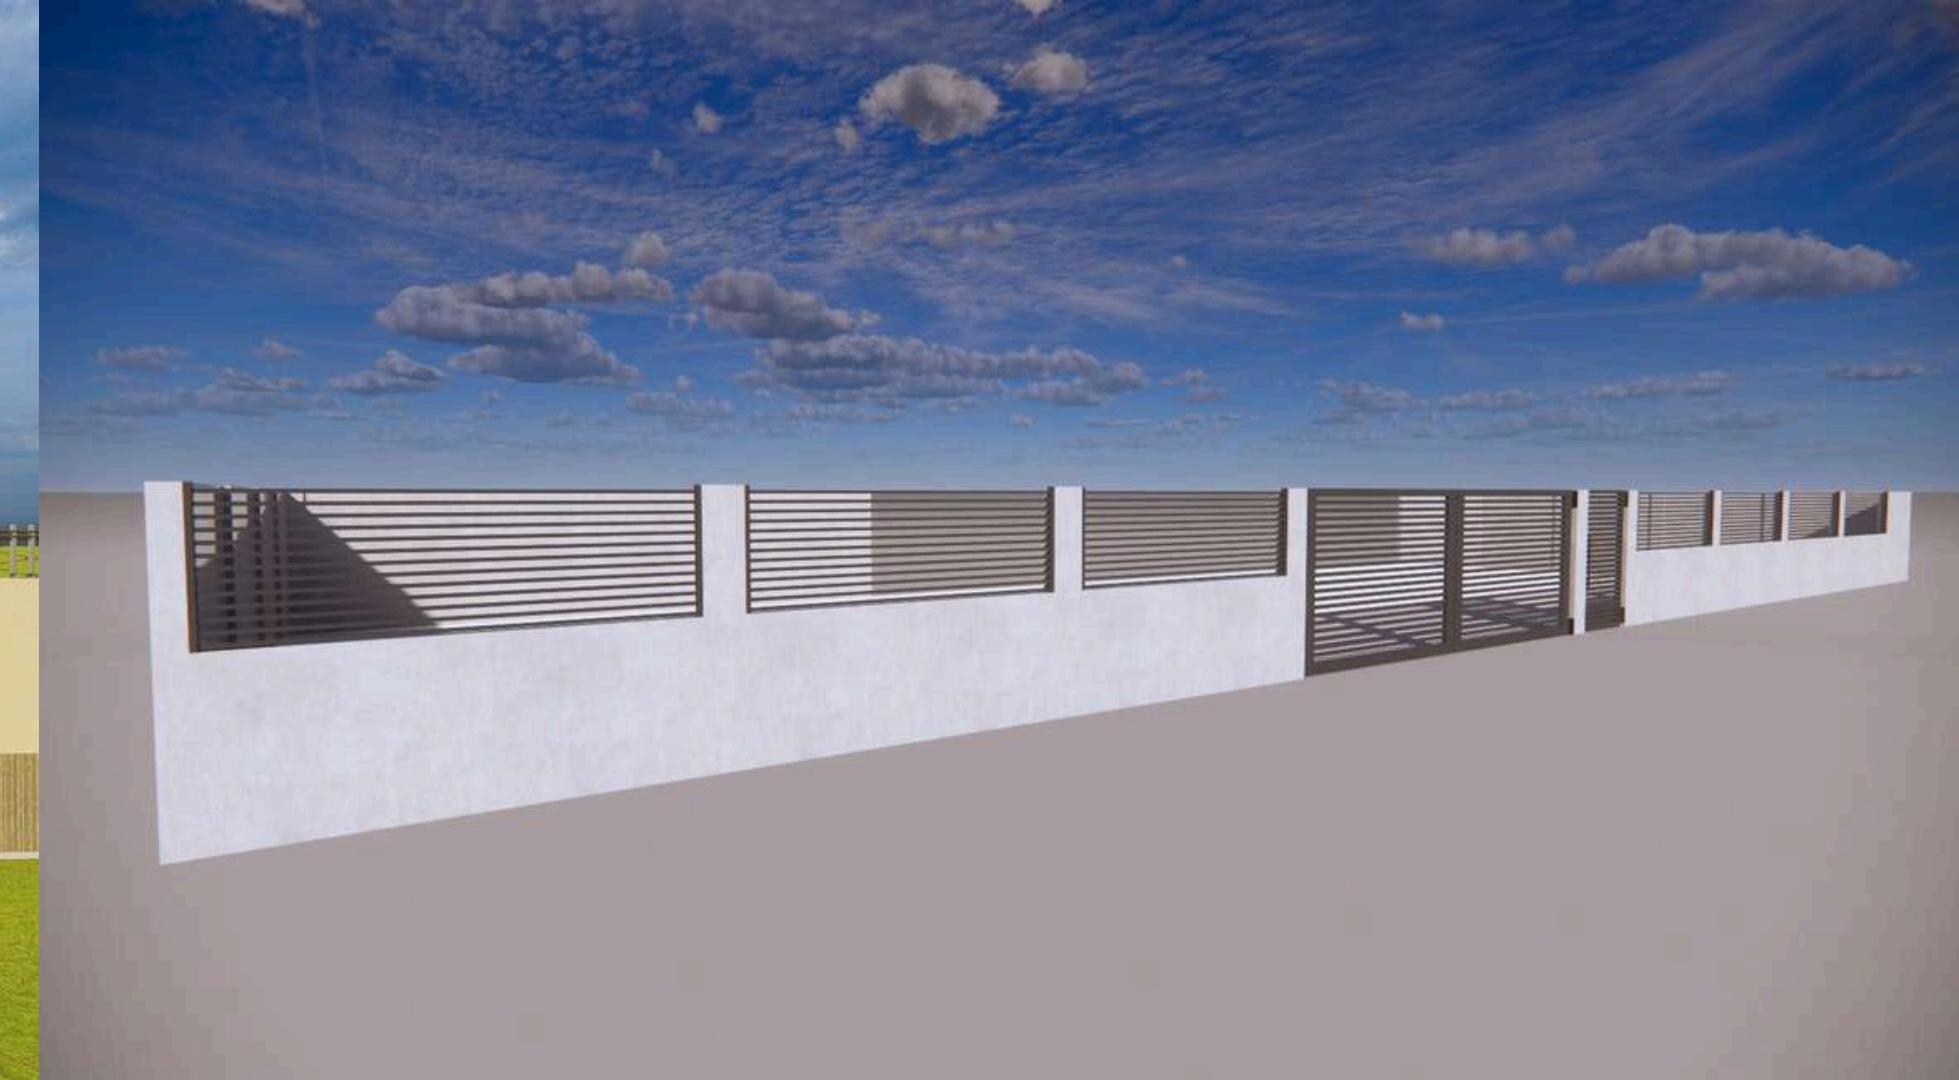

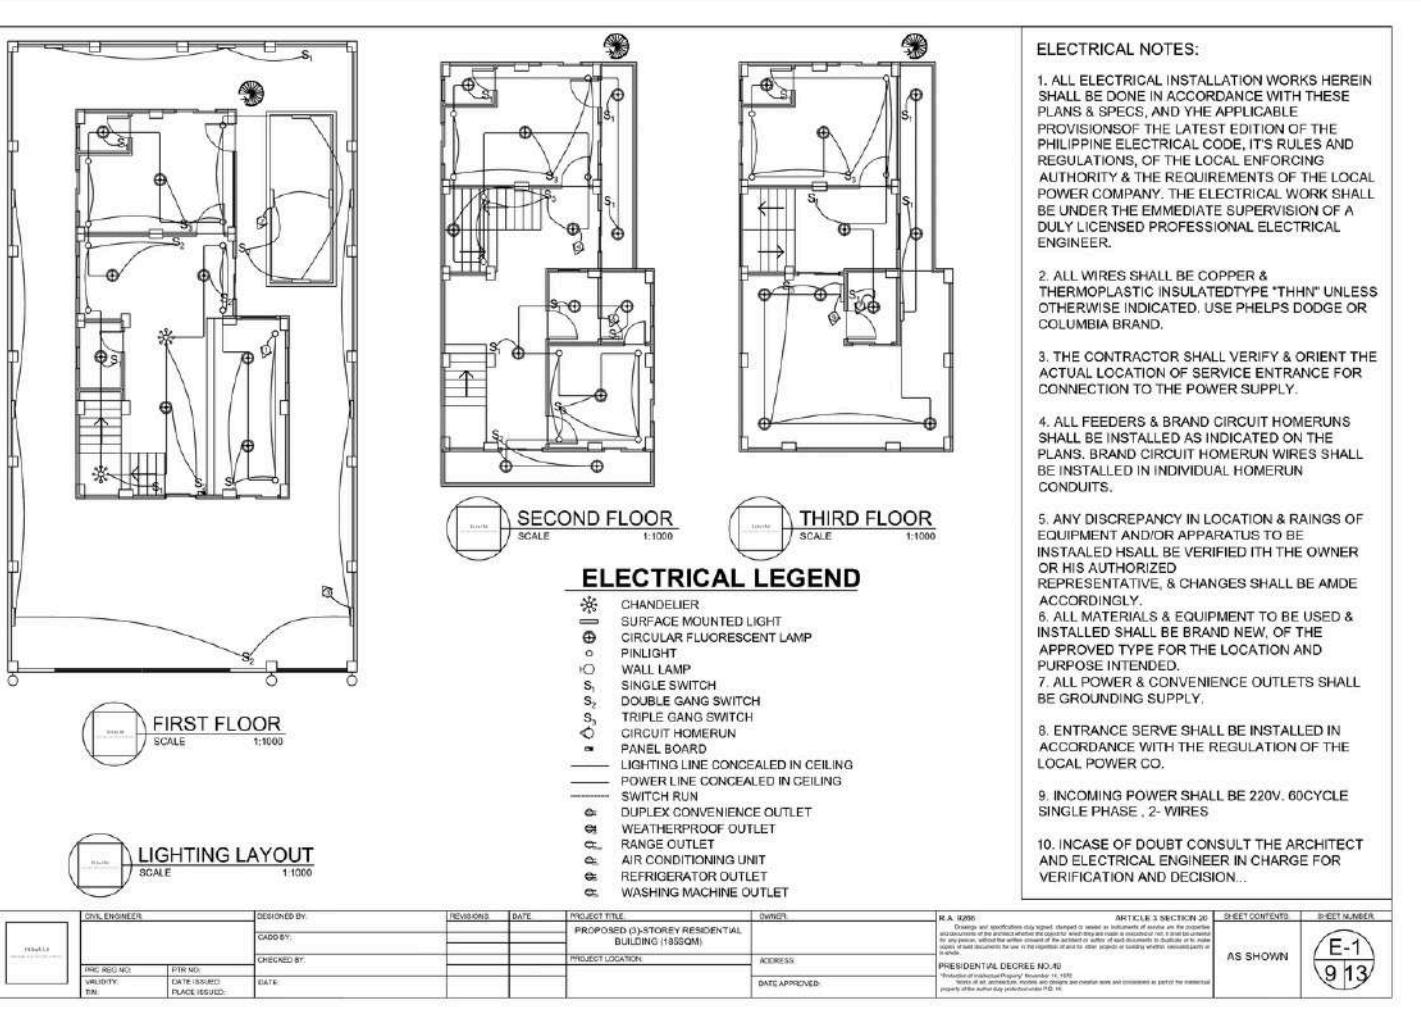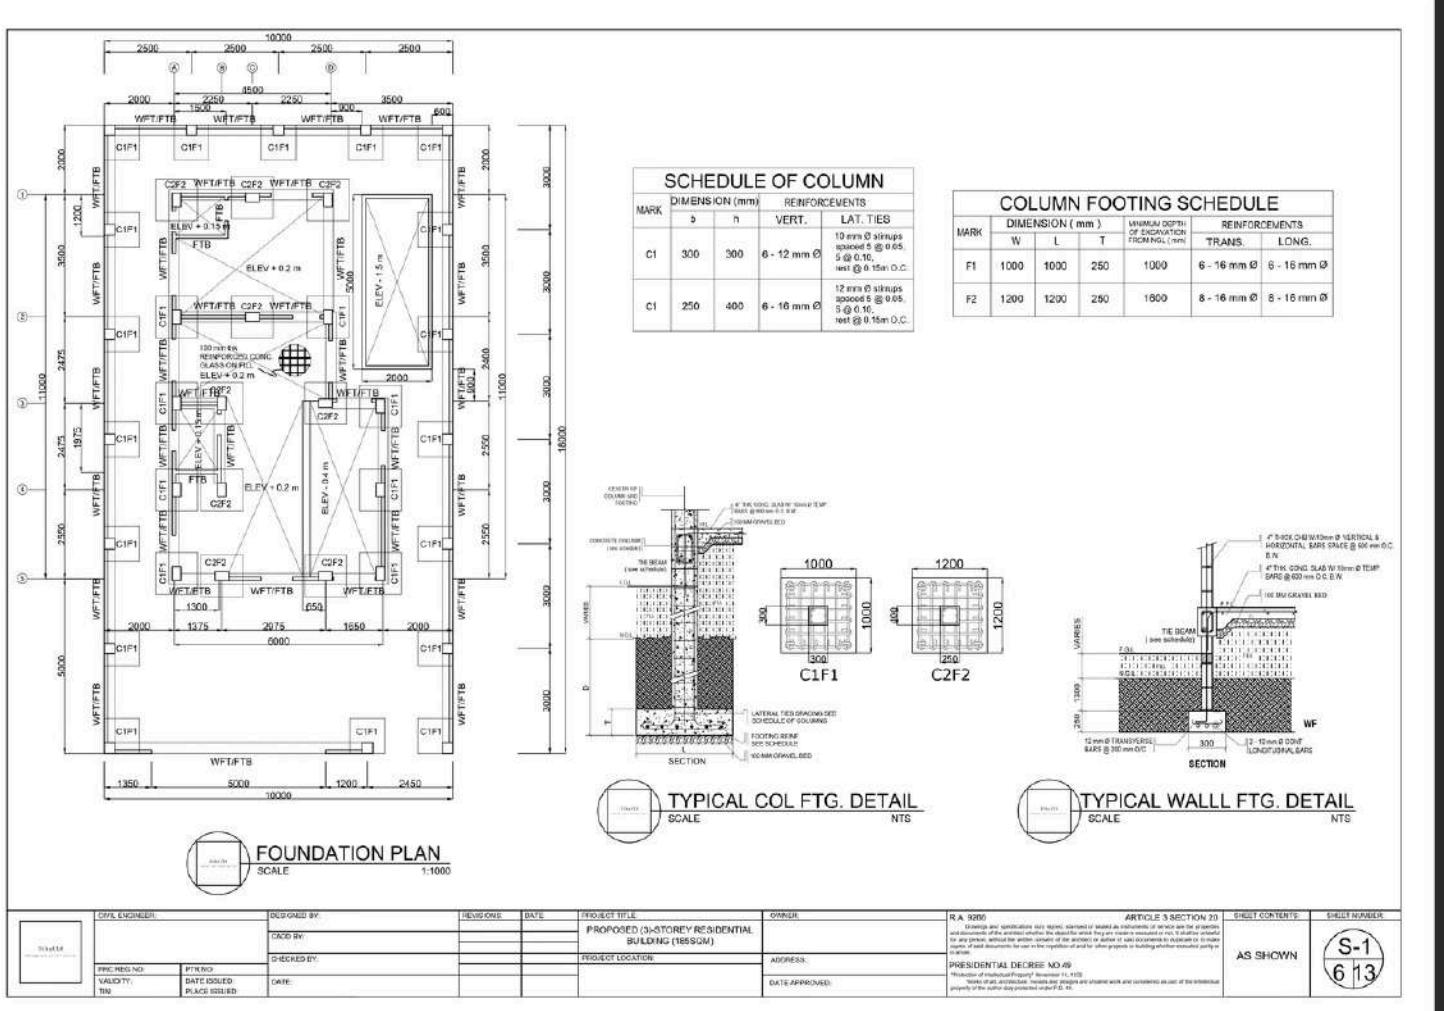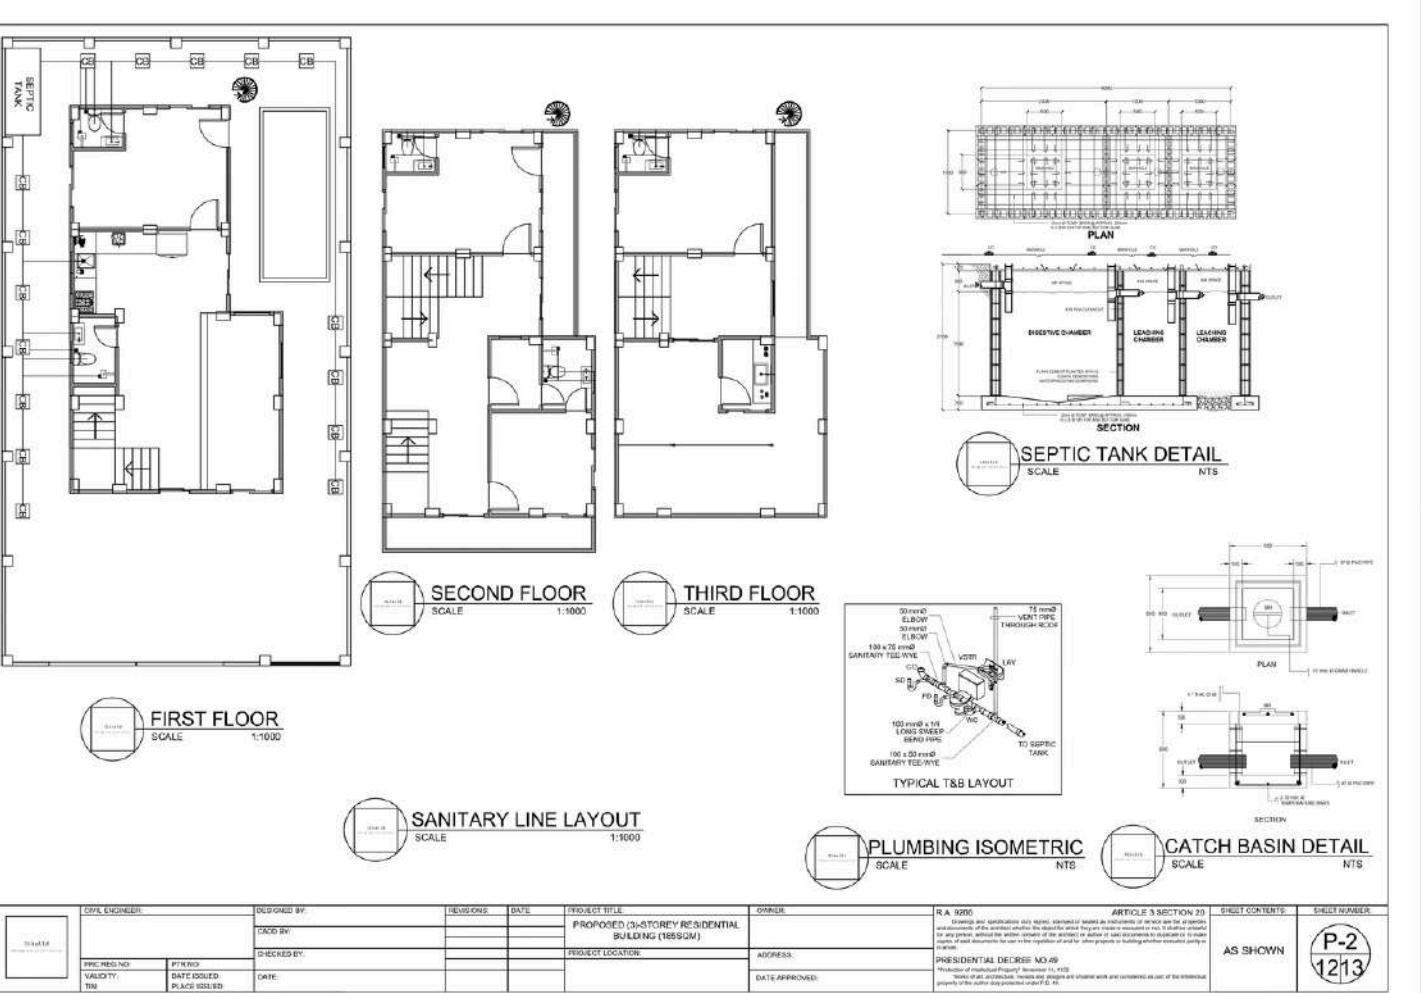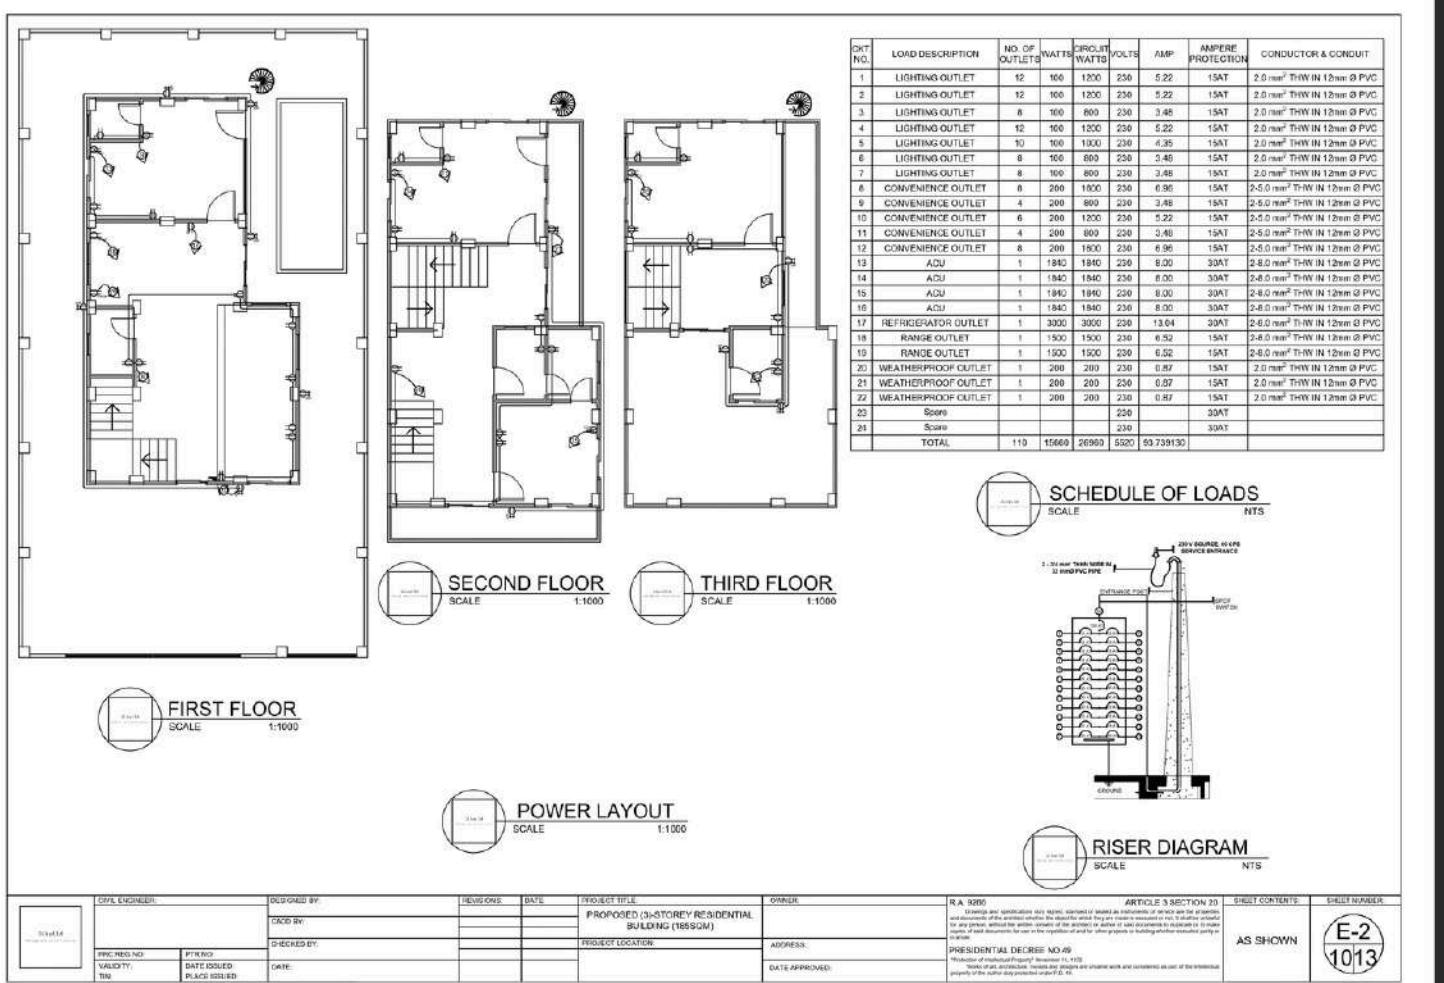



PUBLIC PARK

AREA DEVELOPMENT



FOOD STALLS

DESIGNS

